

煉焦緊急電源系統

煉焦設備檢修課



前言

- 緊急電源系統: 主要在台電側電源供應中斷時，自動啟動緊急發電機電源，當台電側電源恢復供應時，自動轉回台電側，並關閉緊急發電機電源。
- A. T. S 為Automatic Transfer Switch的縮寫:
即電源自動切換開關的簡稱，能在常用電源供應中斷時，自動啟動備用電源(緊急發電機)，將負載切換至備用電源側，而在正常電源恢復供電時，自動再轉回原電源，並關閉備用電源。




大綱


- 一二階煉焦場緊急電源系統
- 三四階煉焦場緊急電源系統
- CDQ 緊急電源系統



一二階煉焦場緊急電源系統

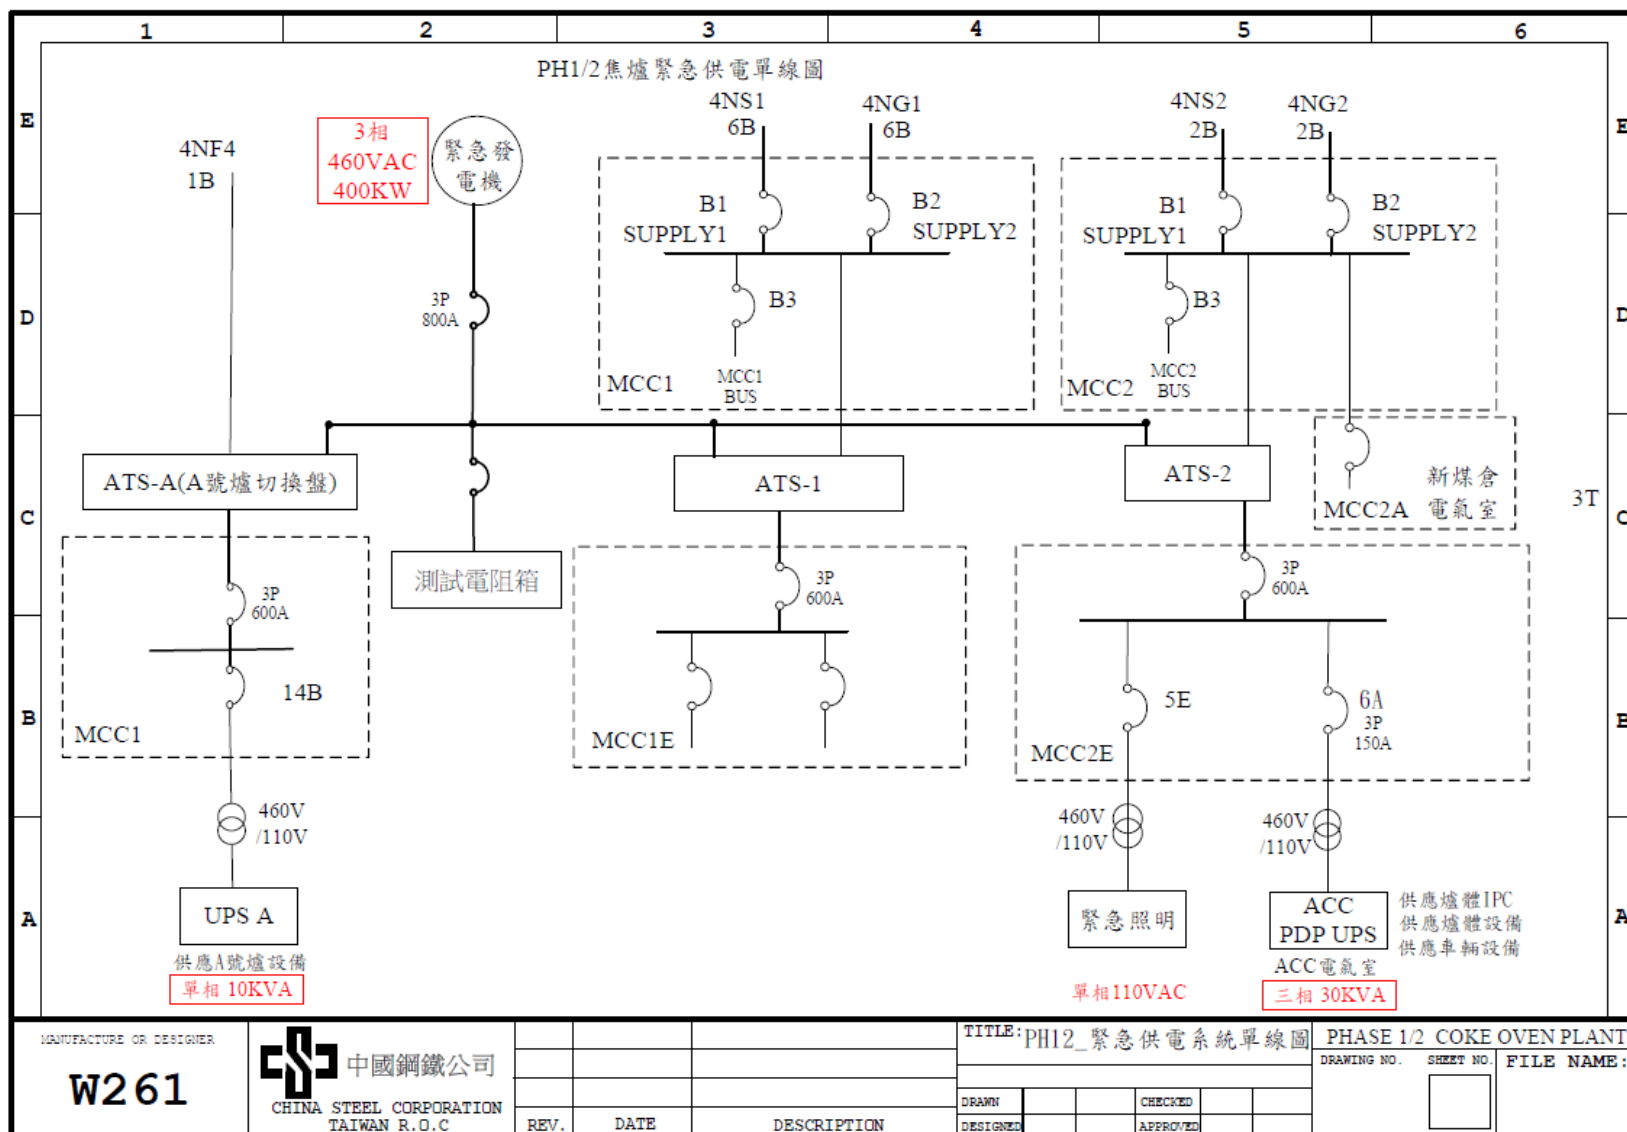

PH12 煉焦UPS-ACC PDP

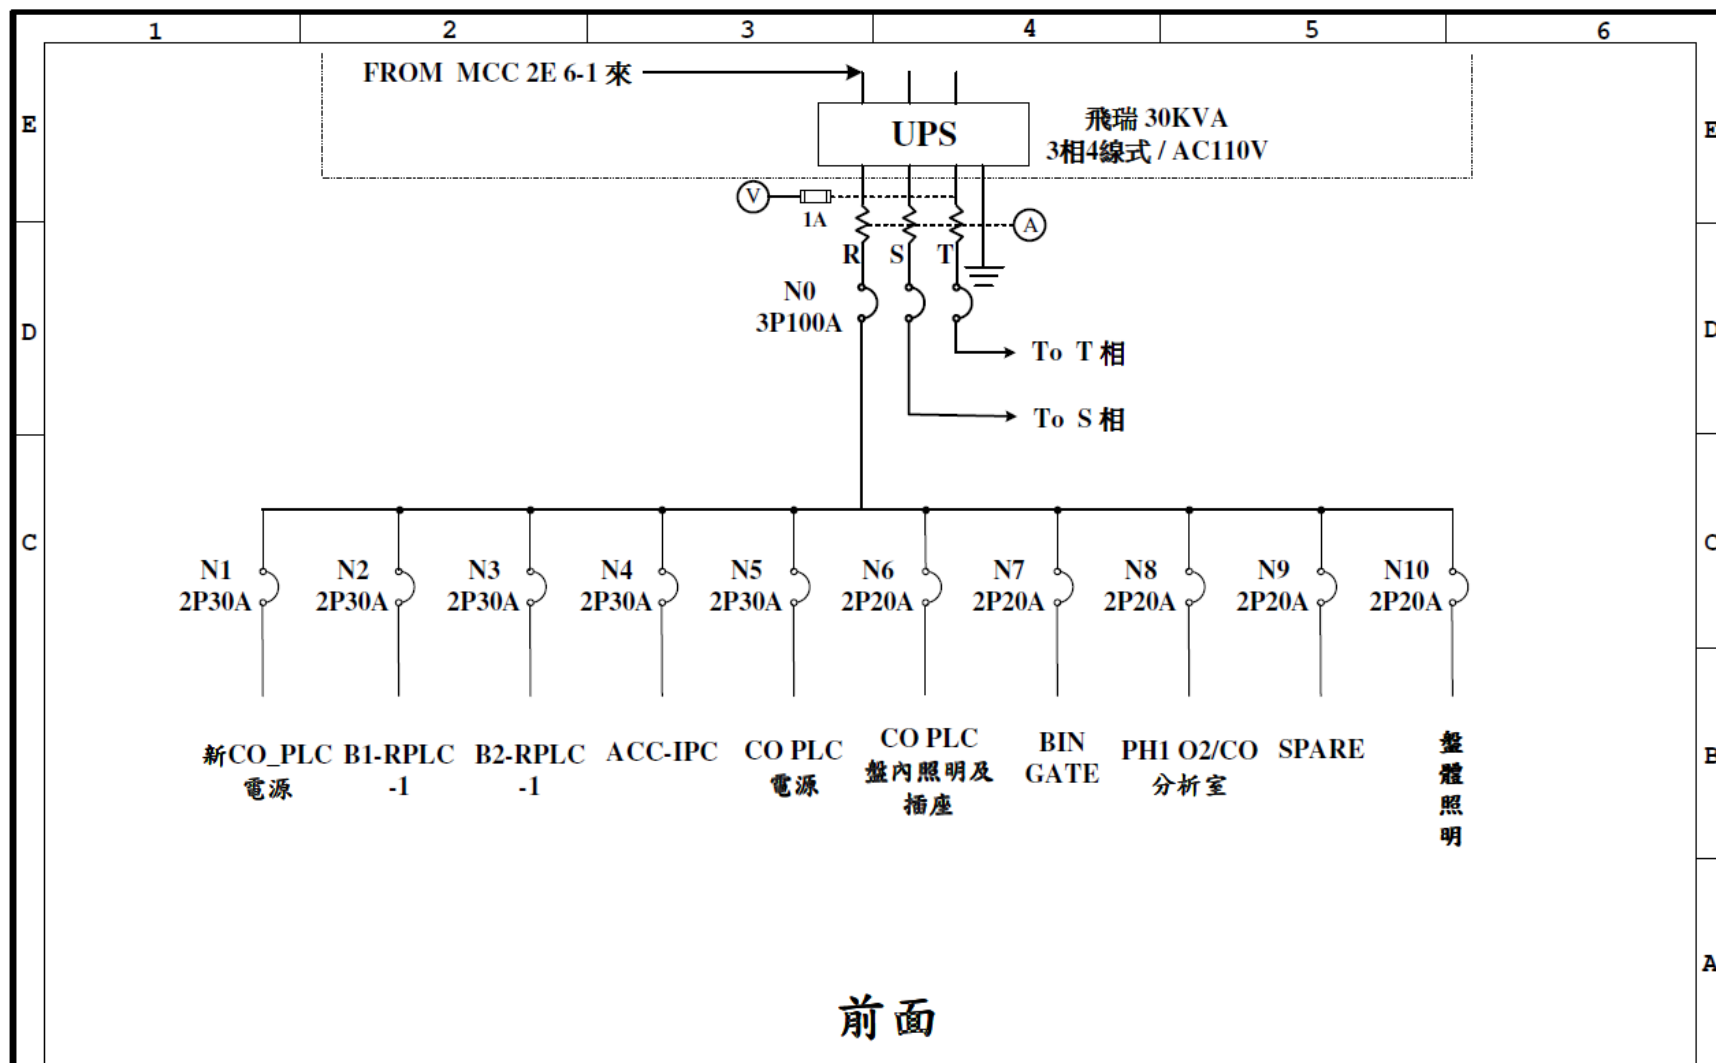

MANUFACTURE OR DESIGNER

W261



中國鋼鐵公司

CHINA STEEL CORPORATION
TAIWAN R.O.C

1.0	95.10.1	
REV.	DATE	DESCRIPTION

TITLE:

一二階PDP電源供應盤單線圖

DRAWN	96.01.05	杜文傑	CHECKED		
DESIGNED	96.01.05	杜文傑	APPROVED		


PHASE 1/2 COKE OVEN PLANT

DRAWING NO. SHEET NO. FILE NAME:

1

PH12_ACC_PDP
單線圖

PH12 煉焦UPS-ACC PDP

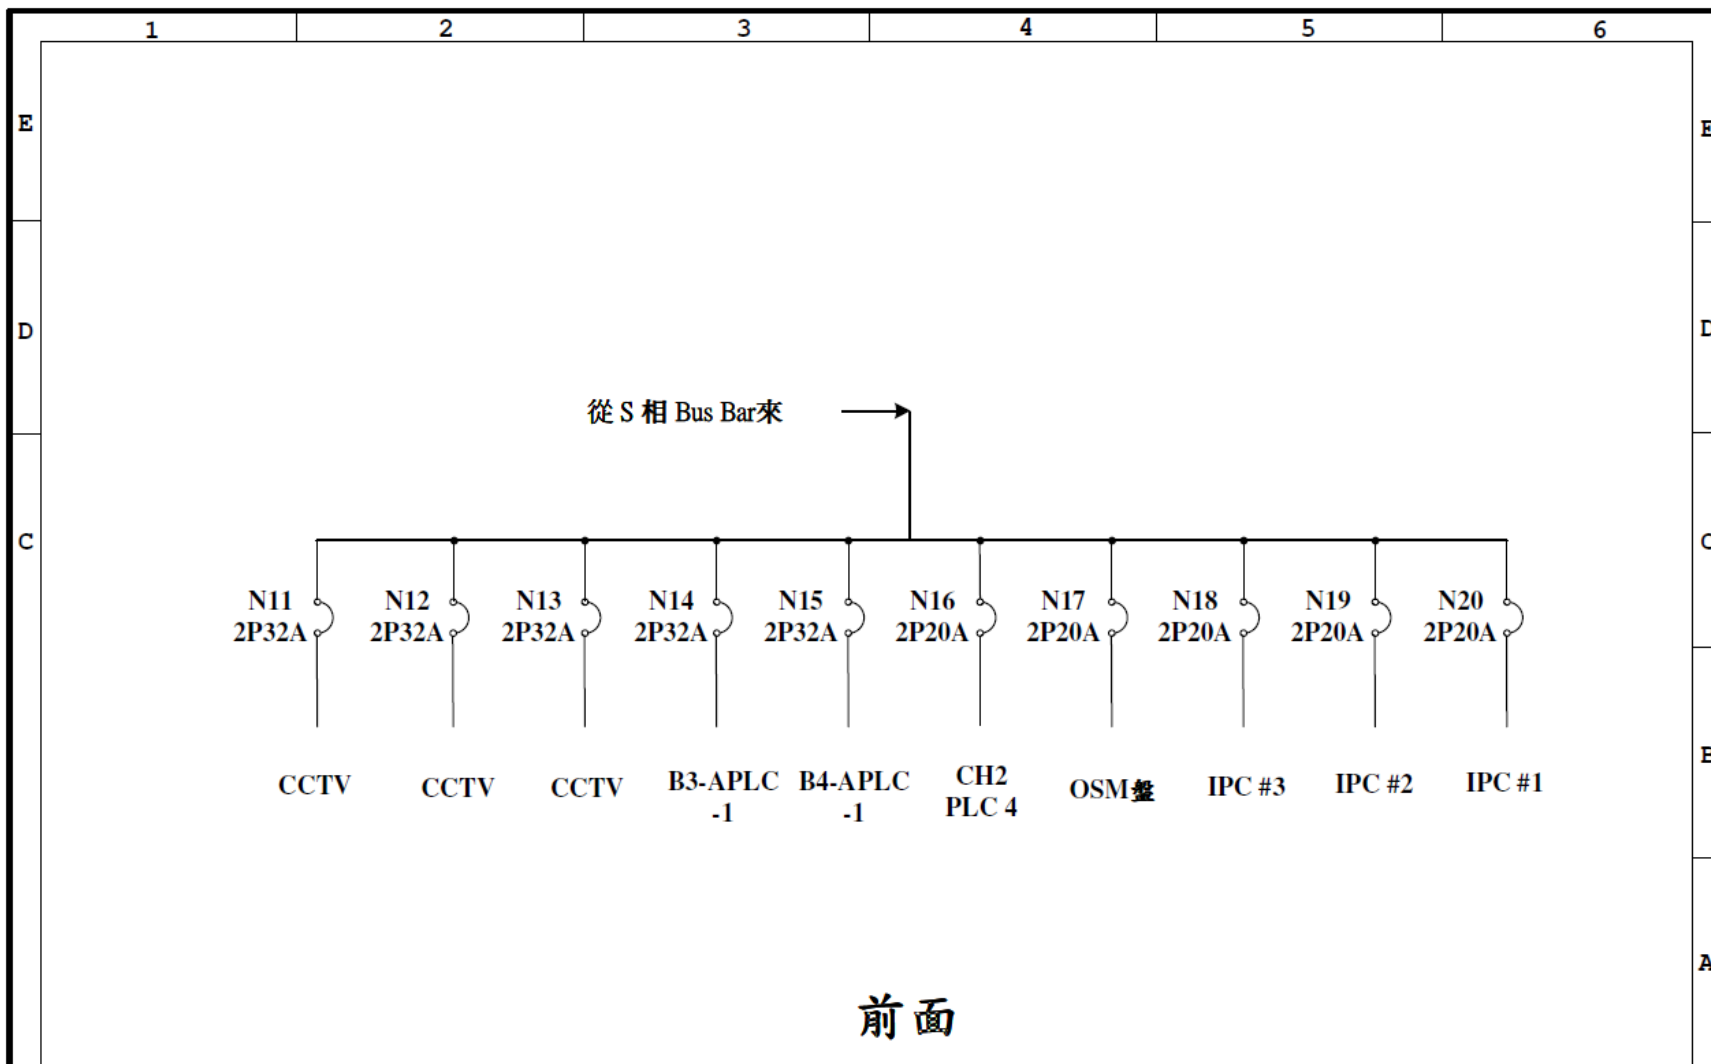

MANUFACTURE OR DESIGNER

W261



中國鋼鐵公司

CHINA STEEL CORPORATION
TAIWAN R.O.C

1.0 95.10.1

REV. DATE

DESCRIPTION

TITLE:

一二階PDP電源供應盤單線圖

DRAWN

96.01.05

杜文傑

CHECKED

96.01.05

杜文傑

APPROVED

PHASE 1/2 COKE OVEN PLANT

DRAWING NO.


SHEET NO.

FILE NAME:

2


PH12_ACC_PDP
單線圖

PH12 煉焦UPS-ACC PDP

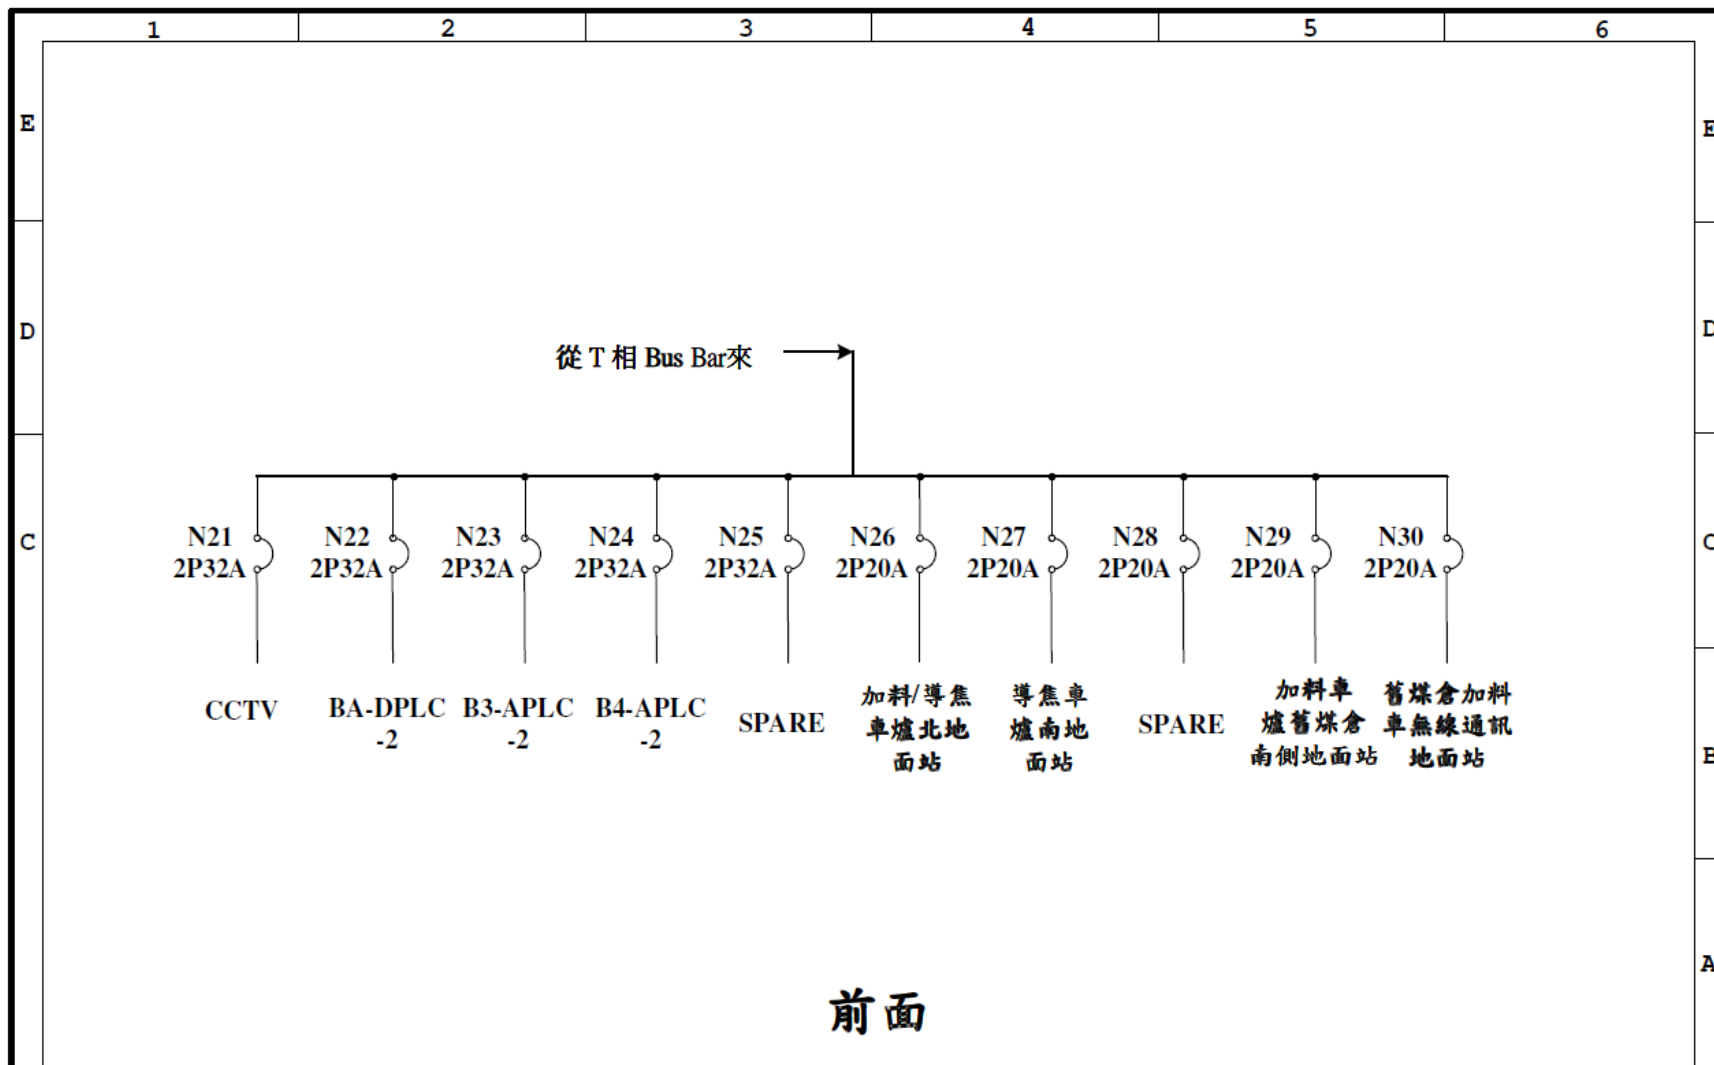


MANUFACTURE OR DESIGNER	 中國鋼鐵公司 CHINA STEEL CORPORATION TAIWAN R.O.C				TITLE: 一二階PDP電源供應盤單線圖				PHASE 1/2 COKE OVEN PLANT		
									DRAWING NO.	SHEET NO.	FILE NAME:
		1.0	95.10.1							3	PH12_ACC_PDP
		REV.	DATE	DESCRIPTION	DRAWN	DESIGNED	CHECKED	APPROVED			單線圖

PH12 煉焦UPS-ACC PDP

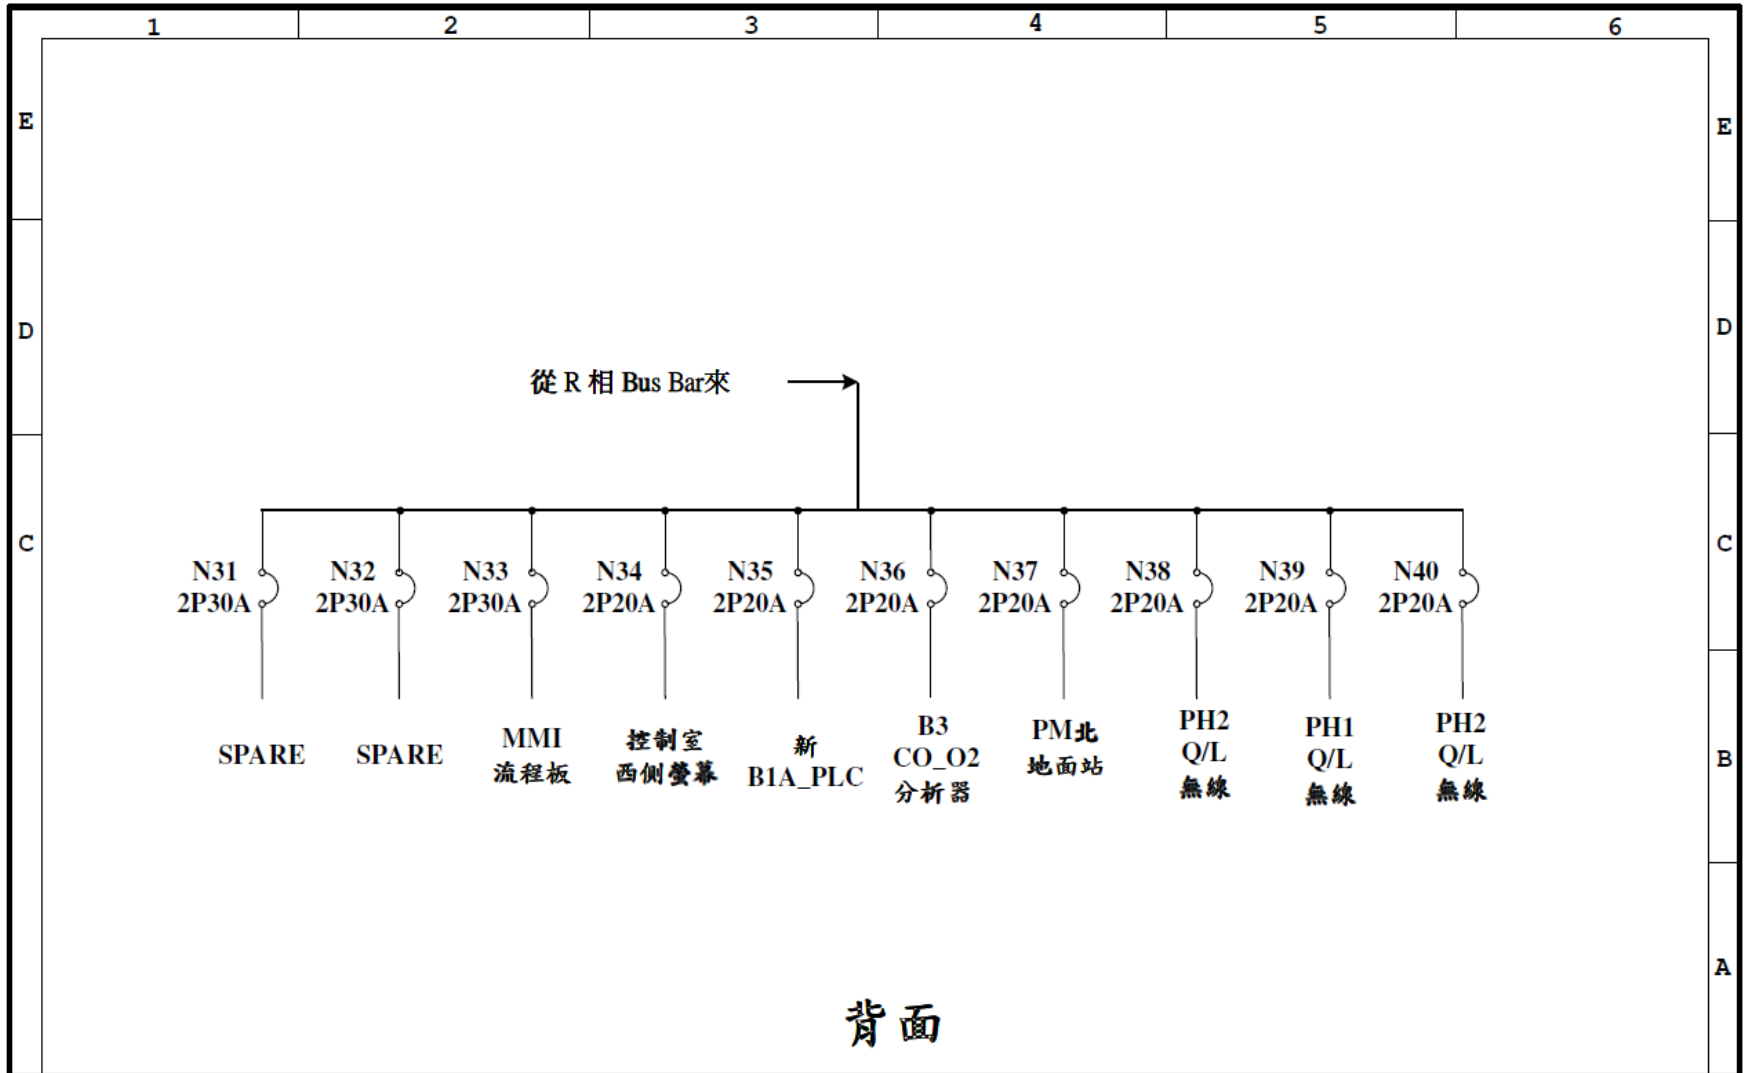


MANUFACTURE OR DESIGNER	 中國鋼鐵公司 CHINA STEEL CORPORATION TAIWAN R.O.C				TITLE:				PHASE 1/2 COKE OVEN PLANT		
					一二階PDP電源供應盤單線圖				DRAWING NO.	SHEET NO.	FILE NAME:
		1.0	95.10.1		DRAWN	96.01.05	杜文傑	CHECKED		4	PH12_ACC_PDP 單線圖
		REV.	DATE	DESCRIPTION	DESIGNED	96.01.05	杜文傑	APPROVED			

PH12 煉焦UPS-ACC PDP

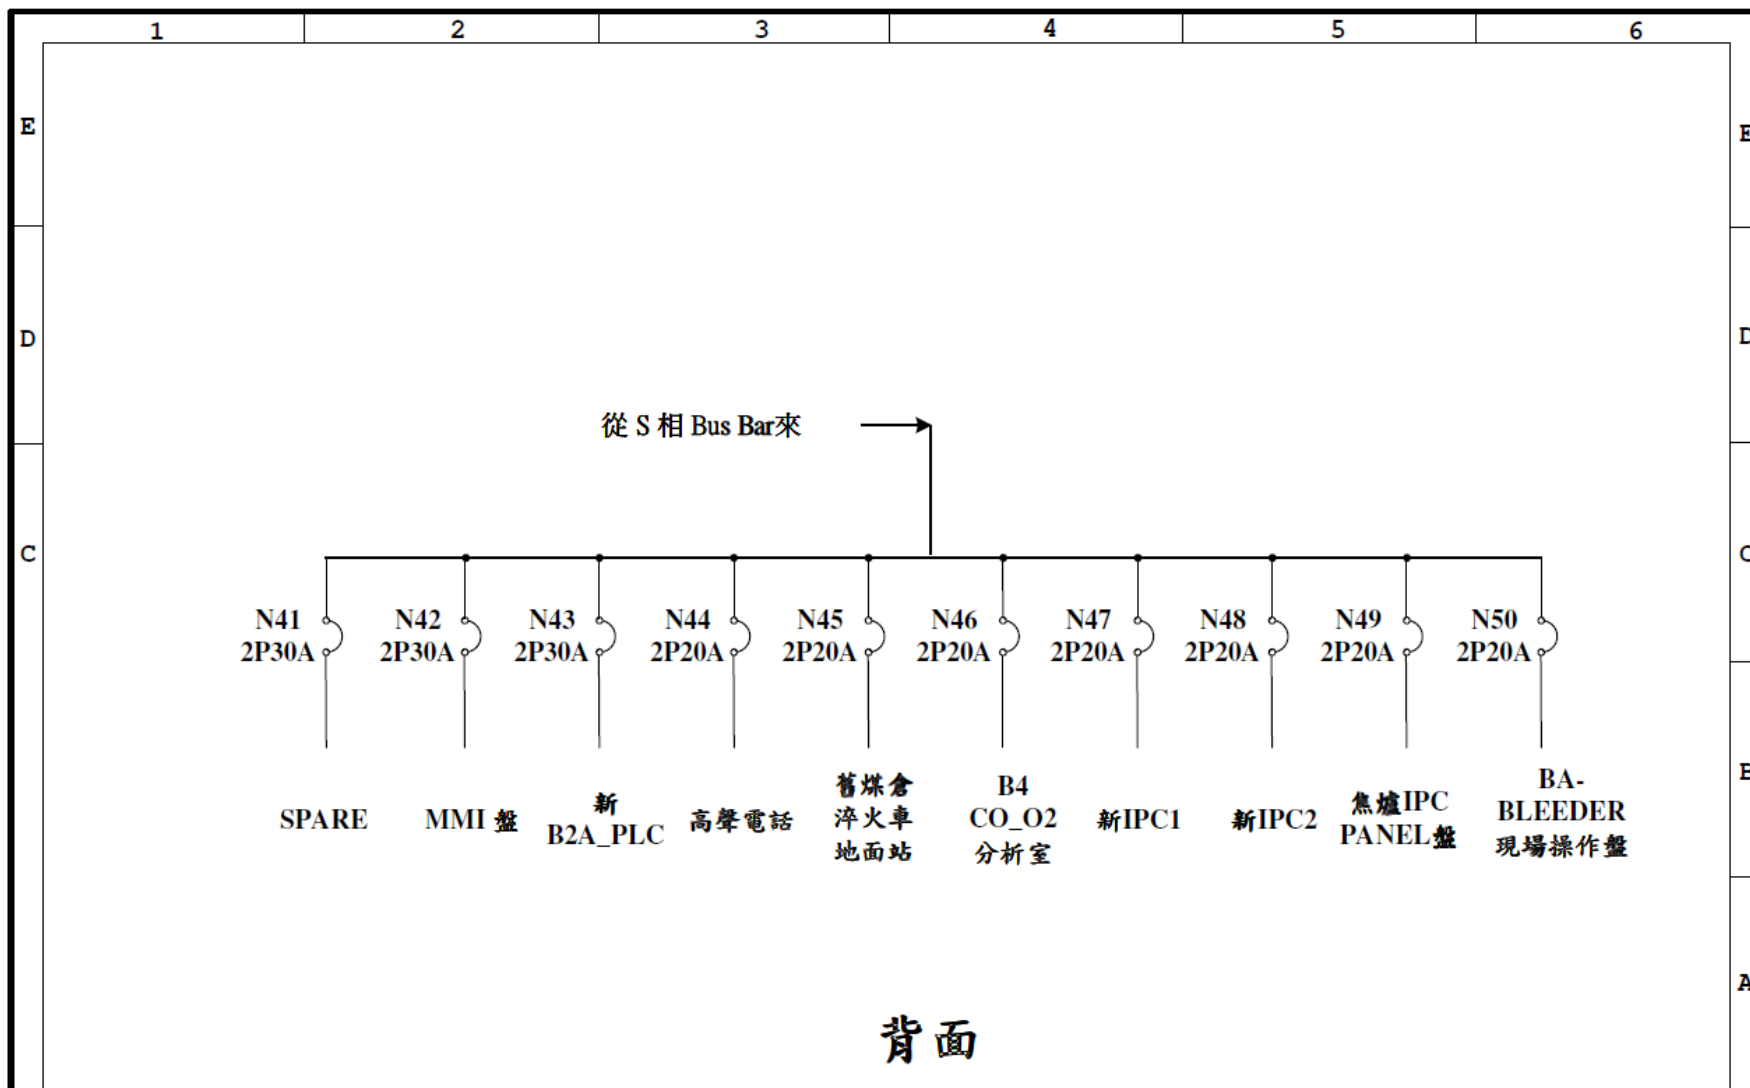

MANUFACTURE OR DESIGNER W261	 中國鋼鐵公司 CHINA STEEL CORPORATION TAIWAN R.O.C				TITLE: 一二階PDP電源供應盤單線圖				PHASE 1/2 COKE OVEN PLANT		
		1.0	95.10.1						DRAWING NO.	SHEET NO.	FILE NAME:
		REV.	DATE	DESCRIPTION	DRAWN	66.01.05	杜文傑	CHECKED		5	PH12_ACC_PDP 單線圖
					DESIGNED	96.01.05	杜文傑	APPROVED			

PH12 煉焦UPS-ACC PDP

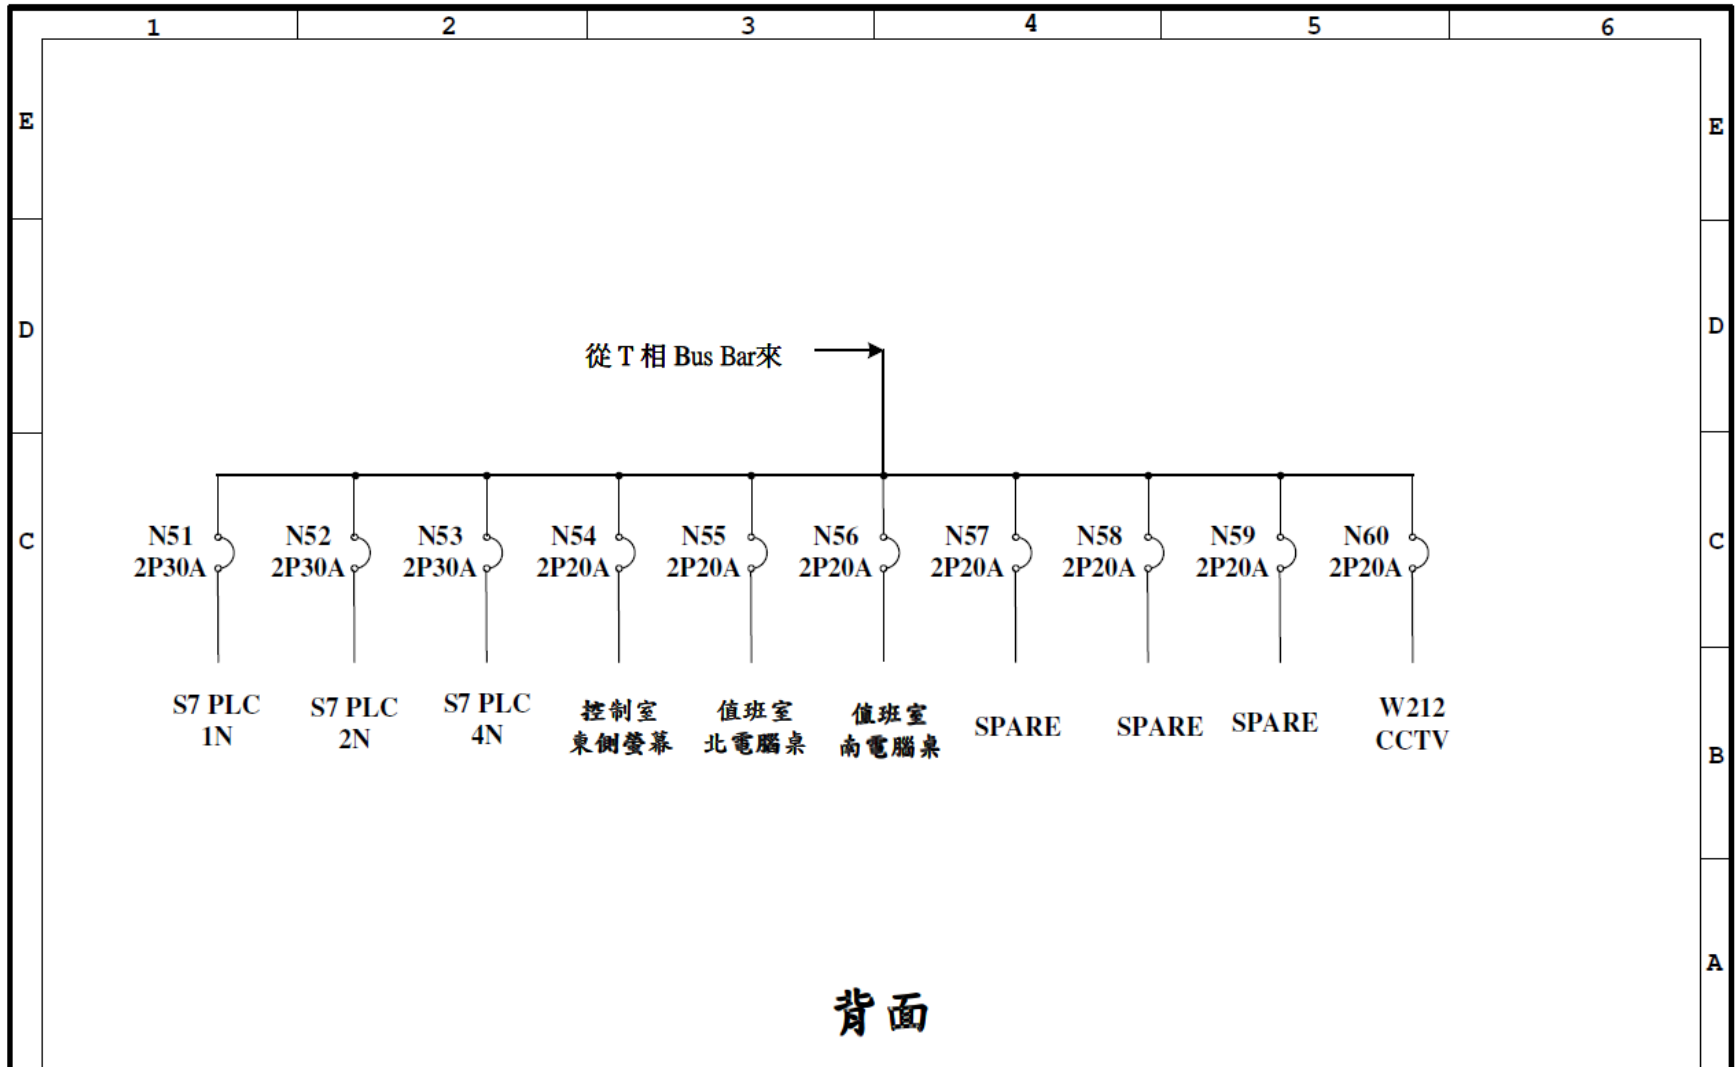

MANUFACTURE OR DESIGNER

W261



中國鋼鐵公司

CHINA STEEL CORPORATION
TAIWAN R.O.C

1.0	95.10.1	
REV.	DATE	DESCRIPTION

TITLE:

一二階PDP電源供應盤單線圖

DRAWN	96.01.05	杜文傑	CHECKED		
DESIGNED	96.01.05	杜文傑	APPROVED		

PHASE 1/2 COKE OVEN PLANT


DRAWING NO. SHEET NO.

FILE NAME:

6


PH12_ACC_PDP
單線圖

PH12 煉焦UPS A

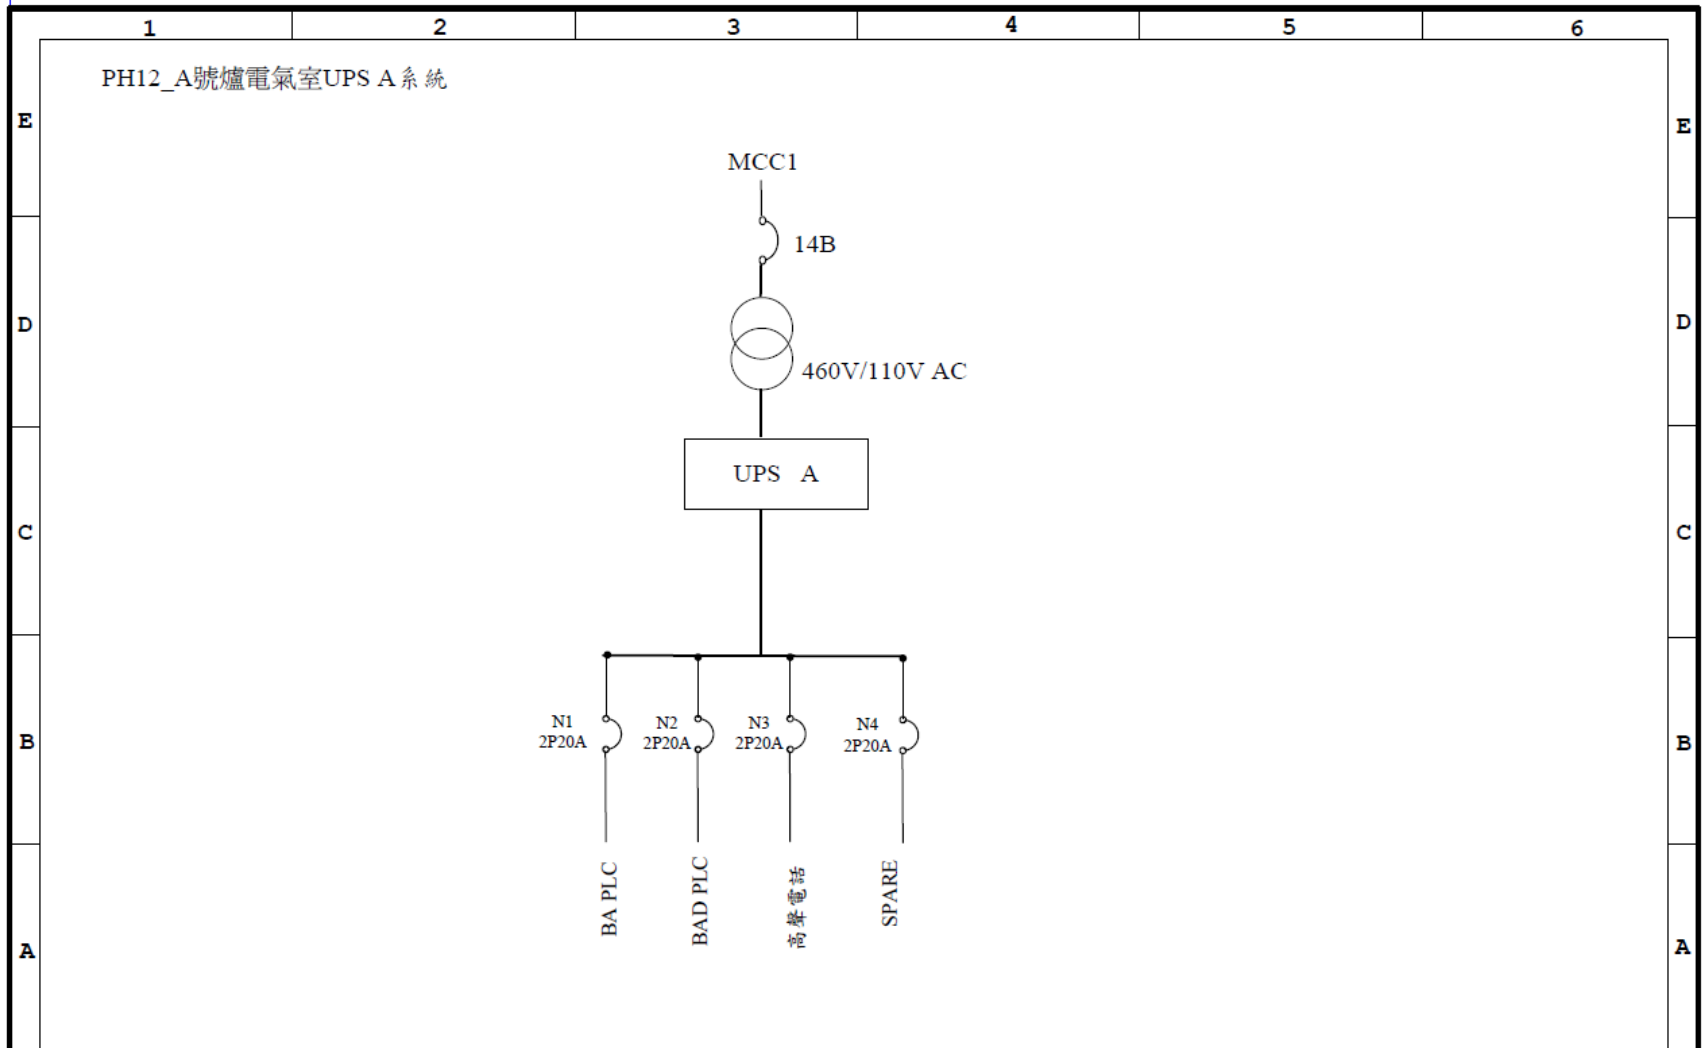

MANUFACTURE OR DESIGNER W261	 中國鋼鐵公司 CHINA STEEL CORPORATION TAIWAN R.O.C			TITLE: PH12_電氣室UPS系統						PHASE 12 COKE OVEN PLANT			
											DRAWING NO.	SHEET NO.	FILE NAME:
					DRAWN	94.12.27	陳光熙	CHECKED			2/6		
					DESIGNED			APPROVED					
		REV.	DATE	DESCRIPTION									

PH34煉焦場緊急電源系統

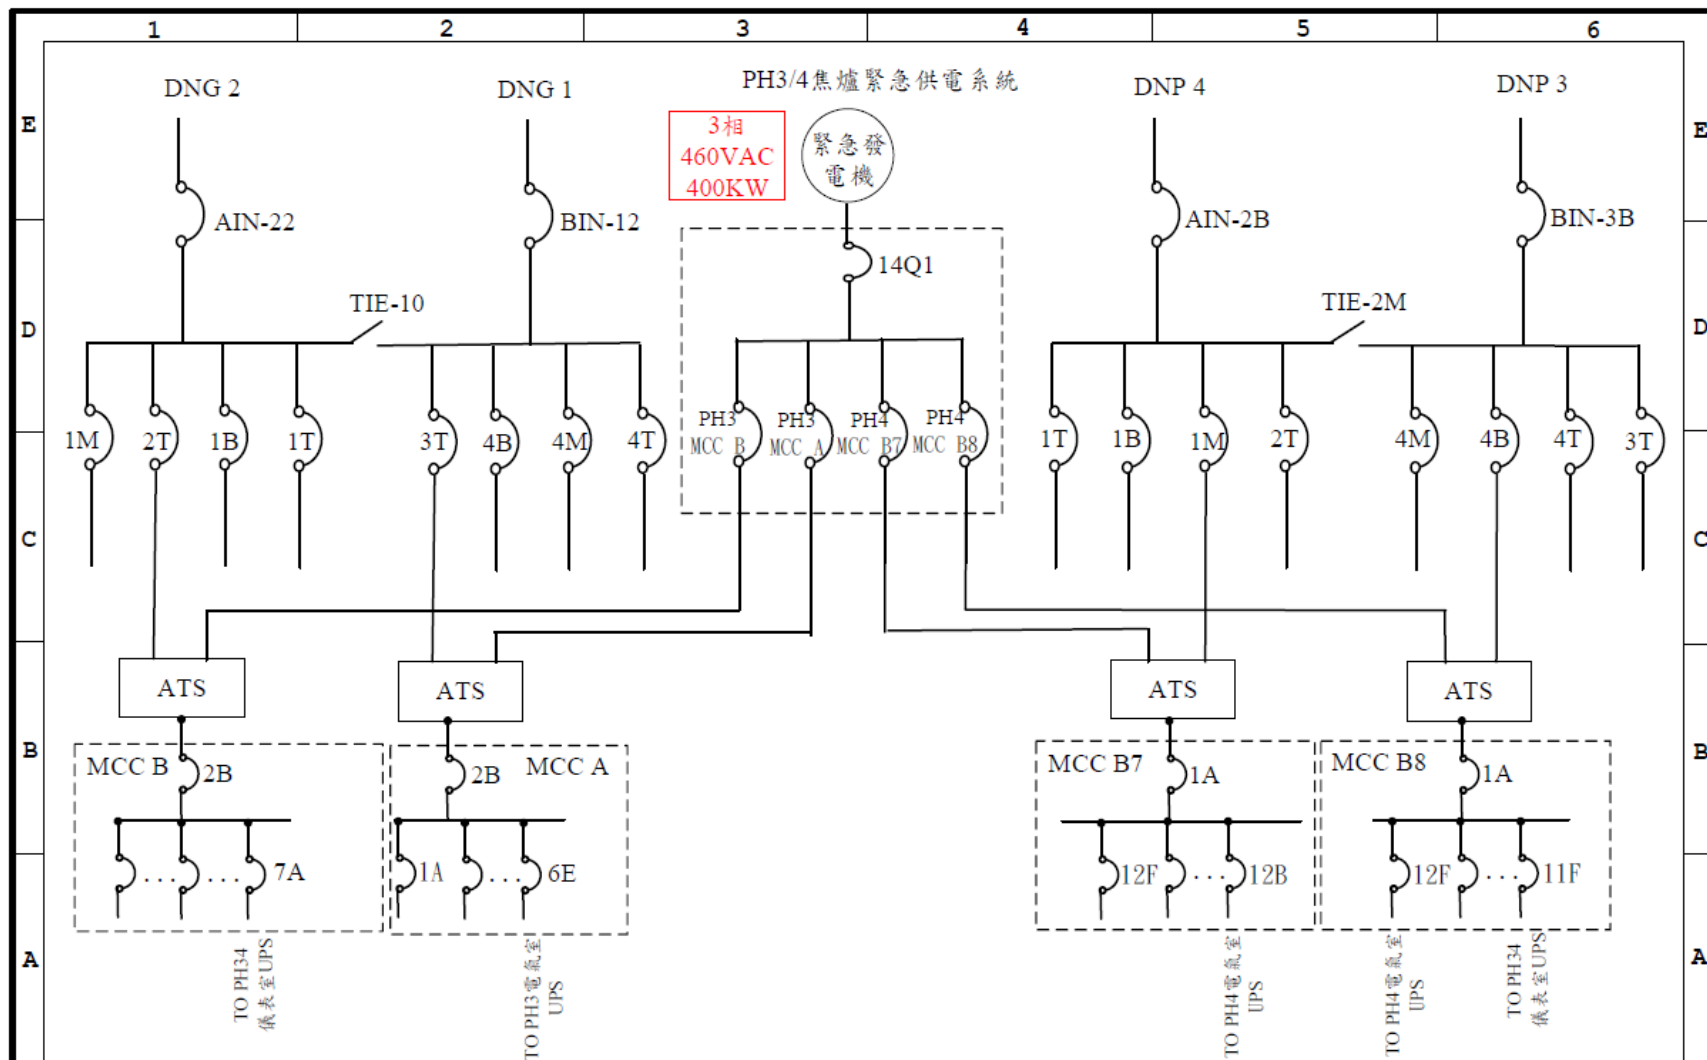

MANUFACTURE OR DESIGNER

W261



中國鋼鐵公司

CHINA STEEL CORPORATION
TAIWAN R.O.C

100.01.14

REV.

DATE

DESCRIPTION

TITLE:

PH34_緊急供電系統單線圖

PHASE 3/4 COKE OVEN PLANT

DRAWING NO.

SHEET NO.

FILE NAME:

DRAWN

94.12.27

陳光熙


CHECKED

DESIGNED


APPROVED

1/6


PH34煉焦儀表室UPS正面

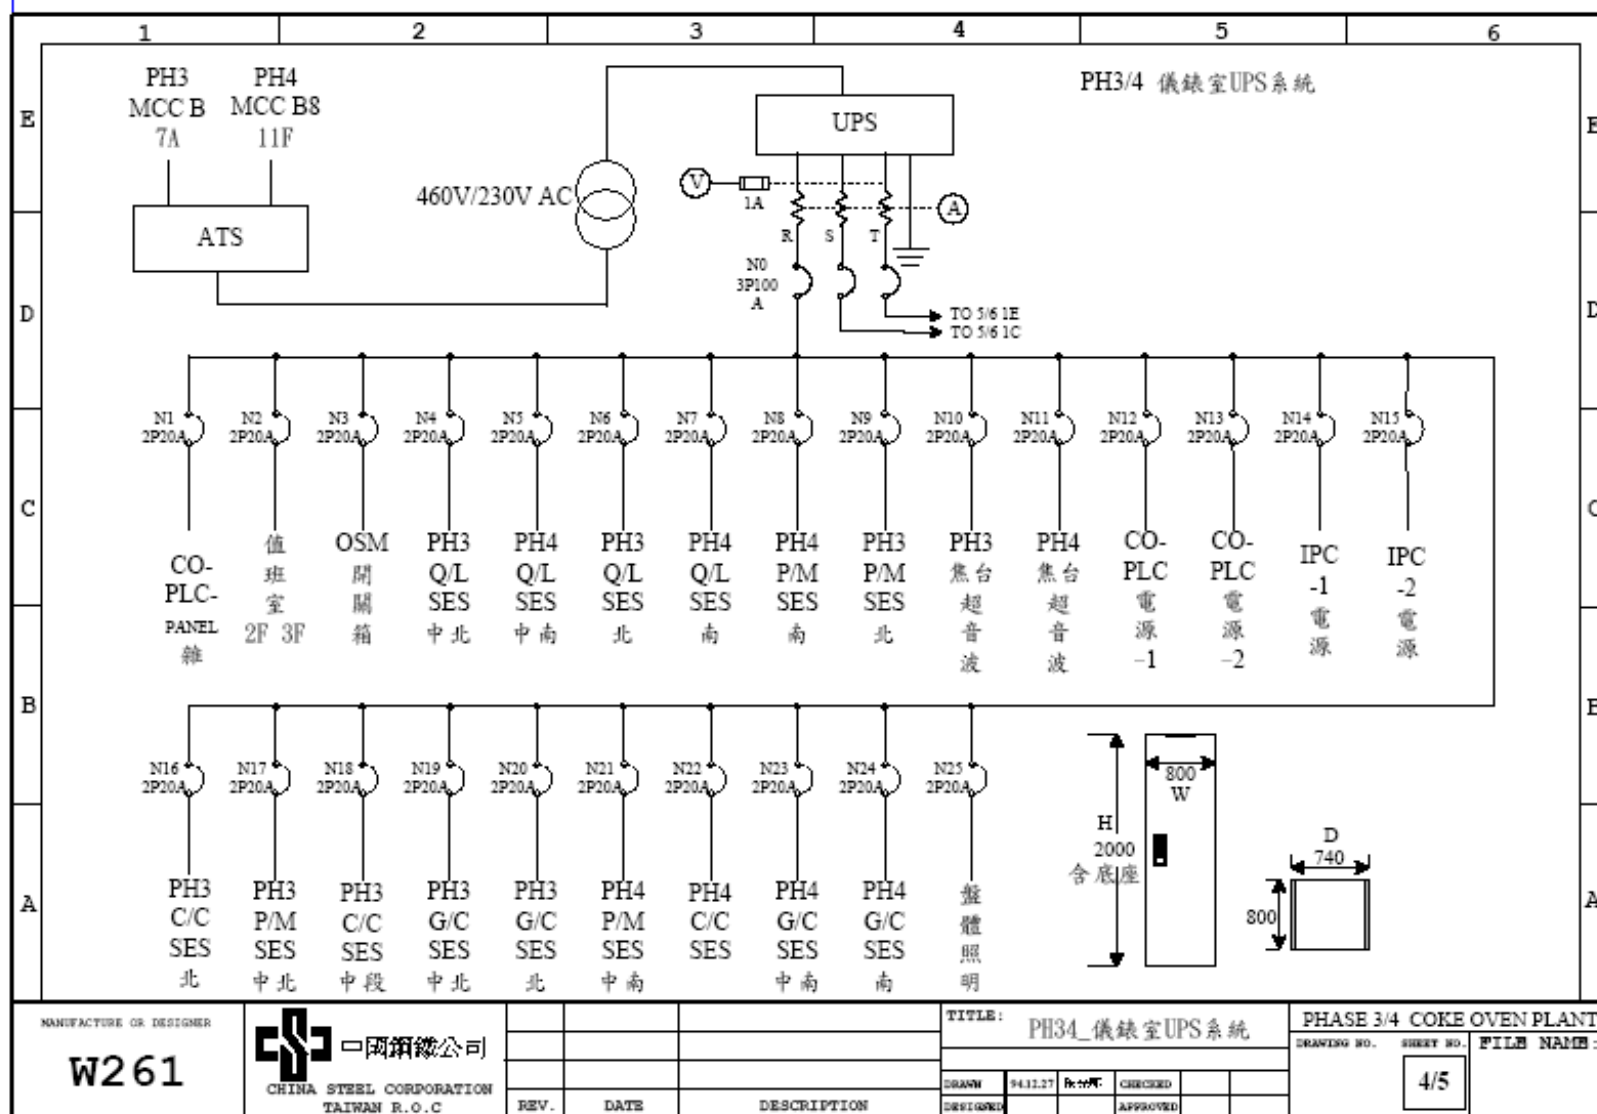

PH34煉焦儀錶室UPS背面

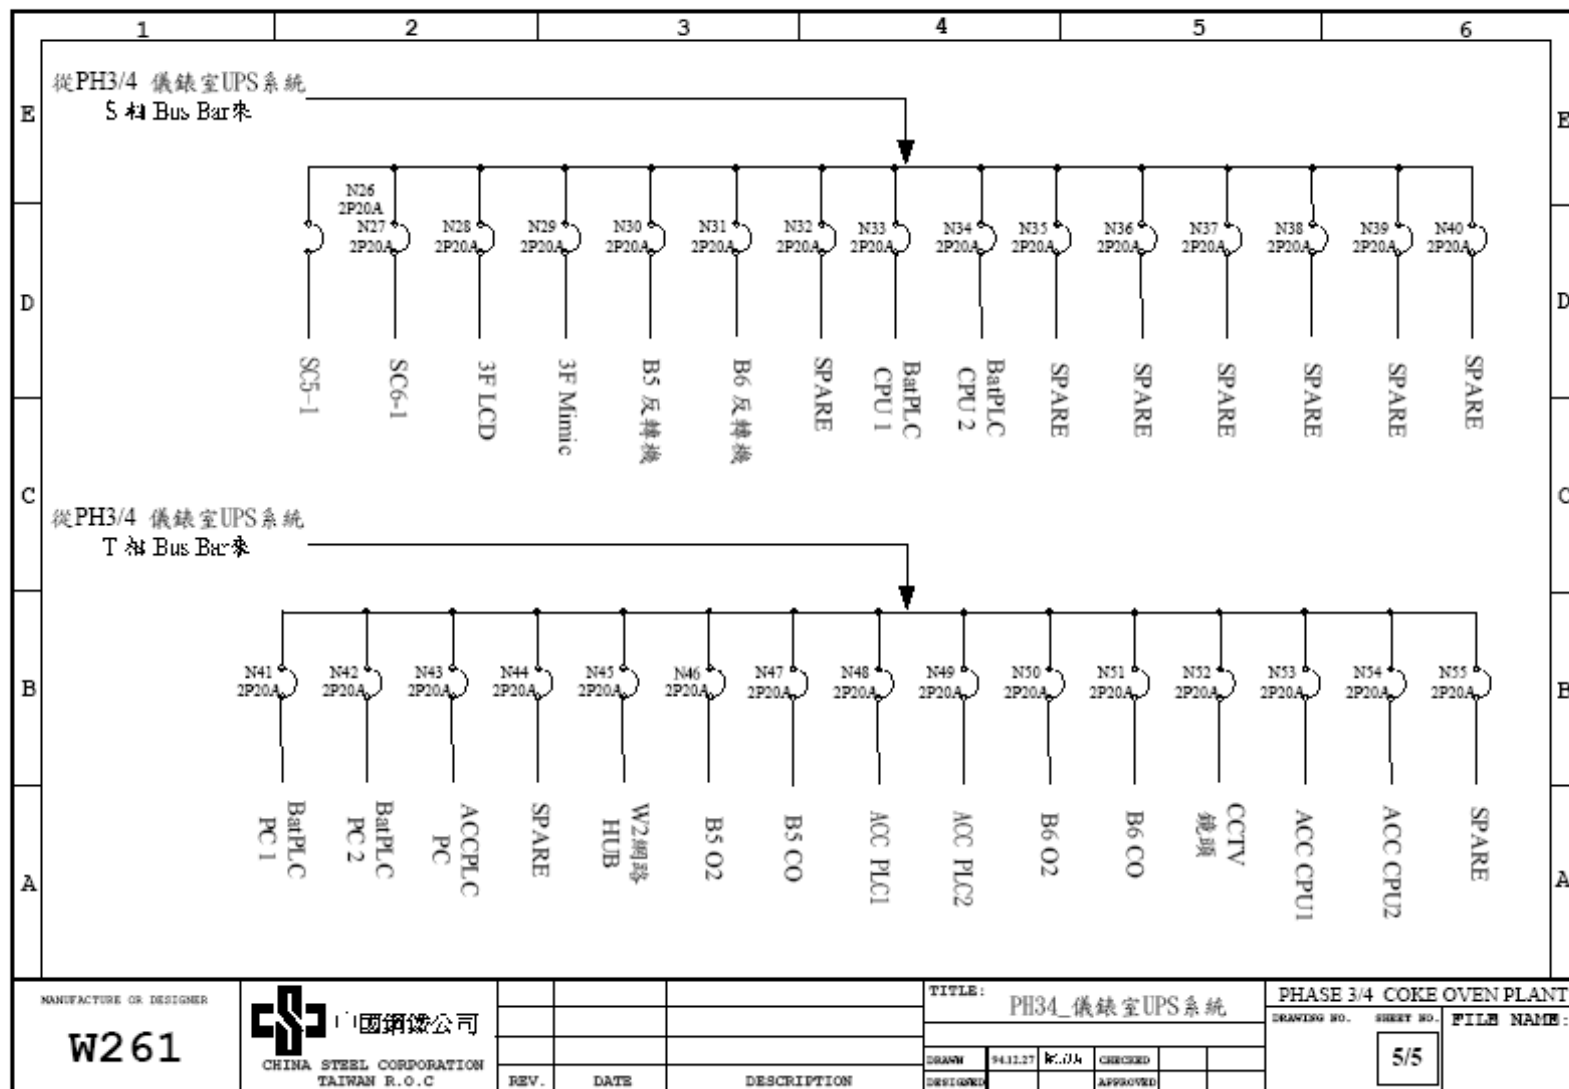

PH4煉焦電氣室UPS

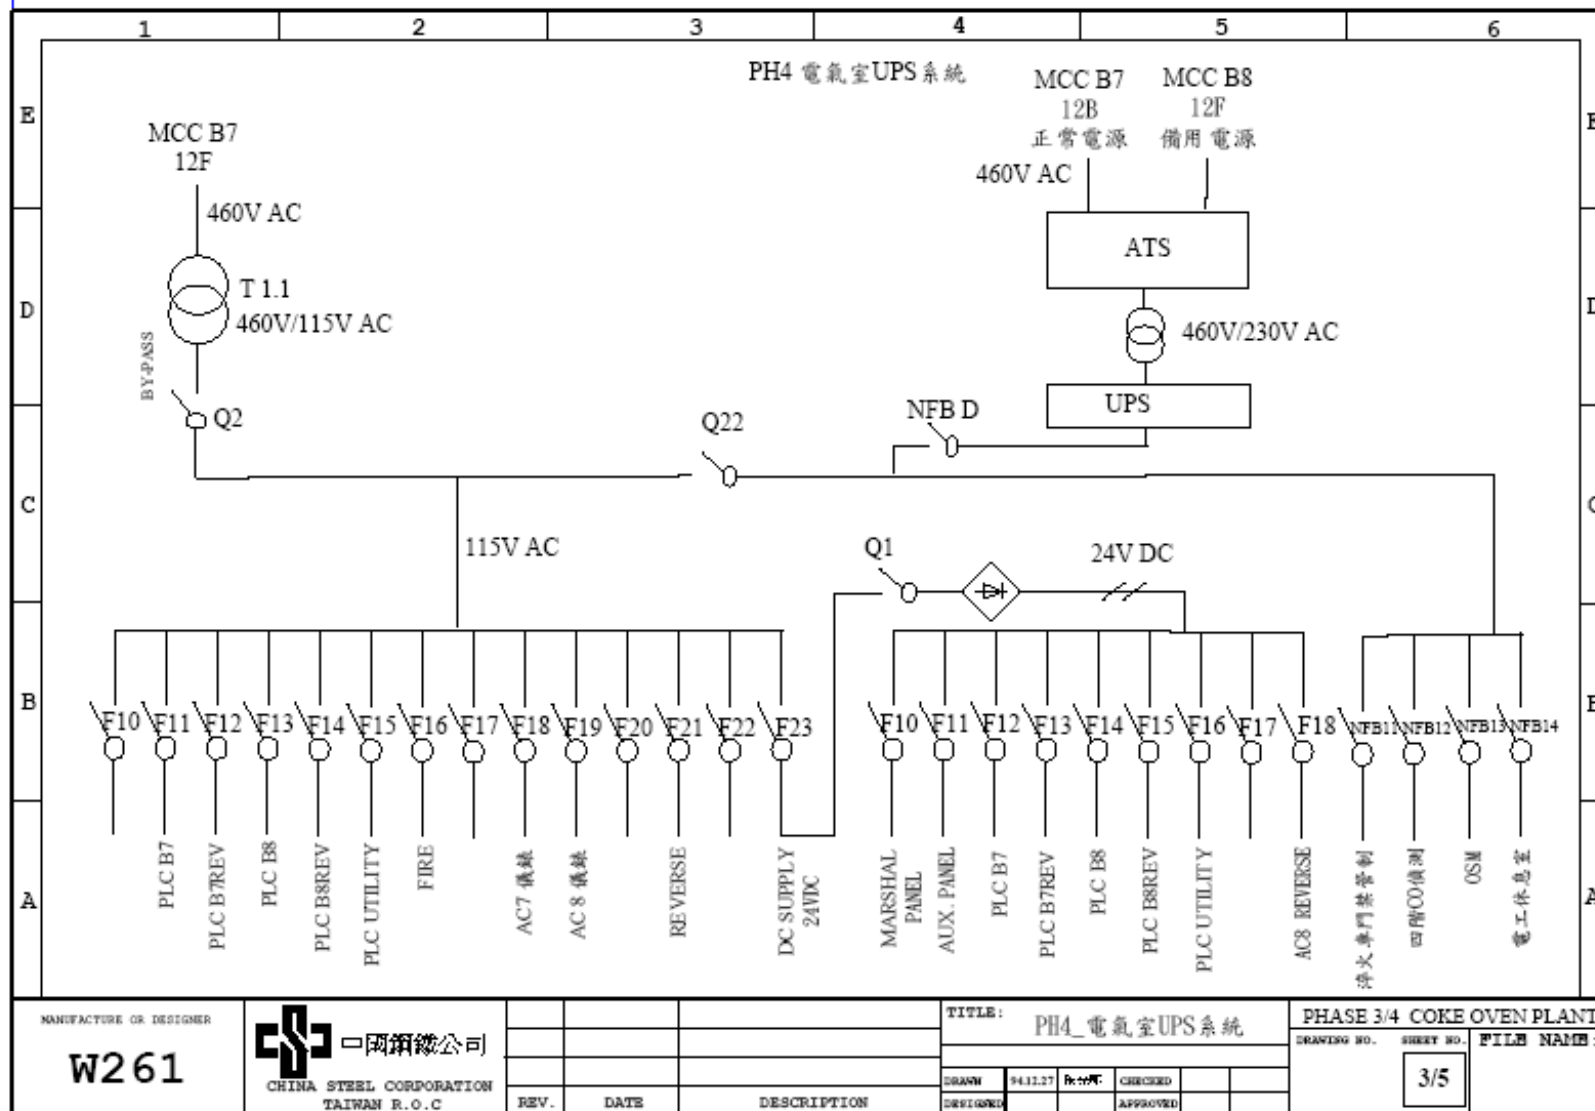

MANUFACTURE OR DESIGNER

W261

中國鋼鐵公司

CHINA STEEL CORPORATION
TAIWAN R.O.C

REV.	DATE	DESCRIPTION


TITLE: PH4_電氣室UPS系統

DRAWN	94.12.27	Rev. 01	CHECKED		
DESIGNED			APPROVED		

PHASE 3/4 COKE OVEN PLANT

DRAWING NO.	SHEET NO.	FILE NAME:
	3/5	

PH3 CDQ緊急電源系統

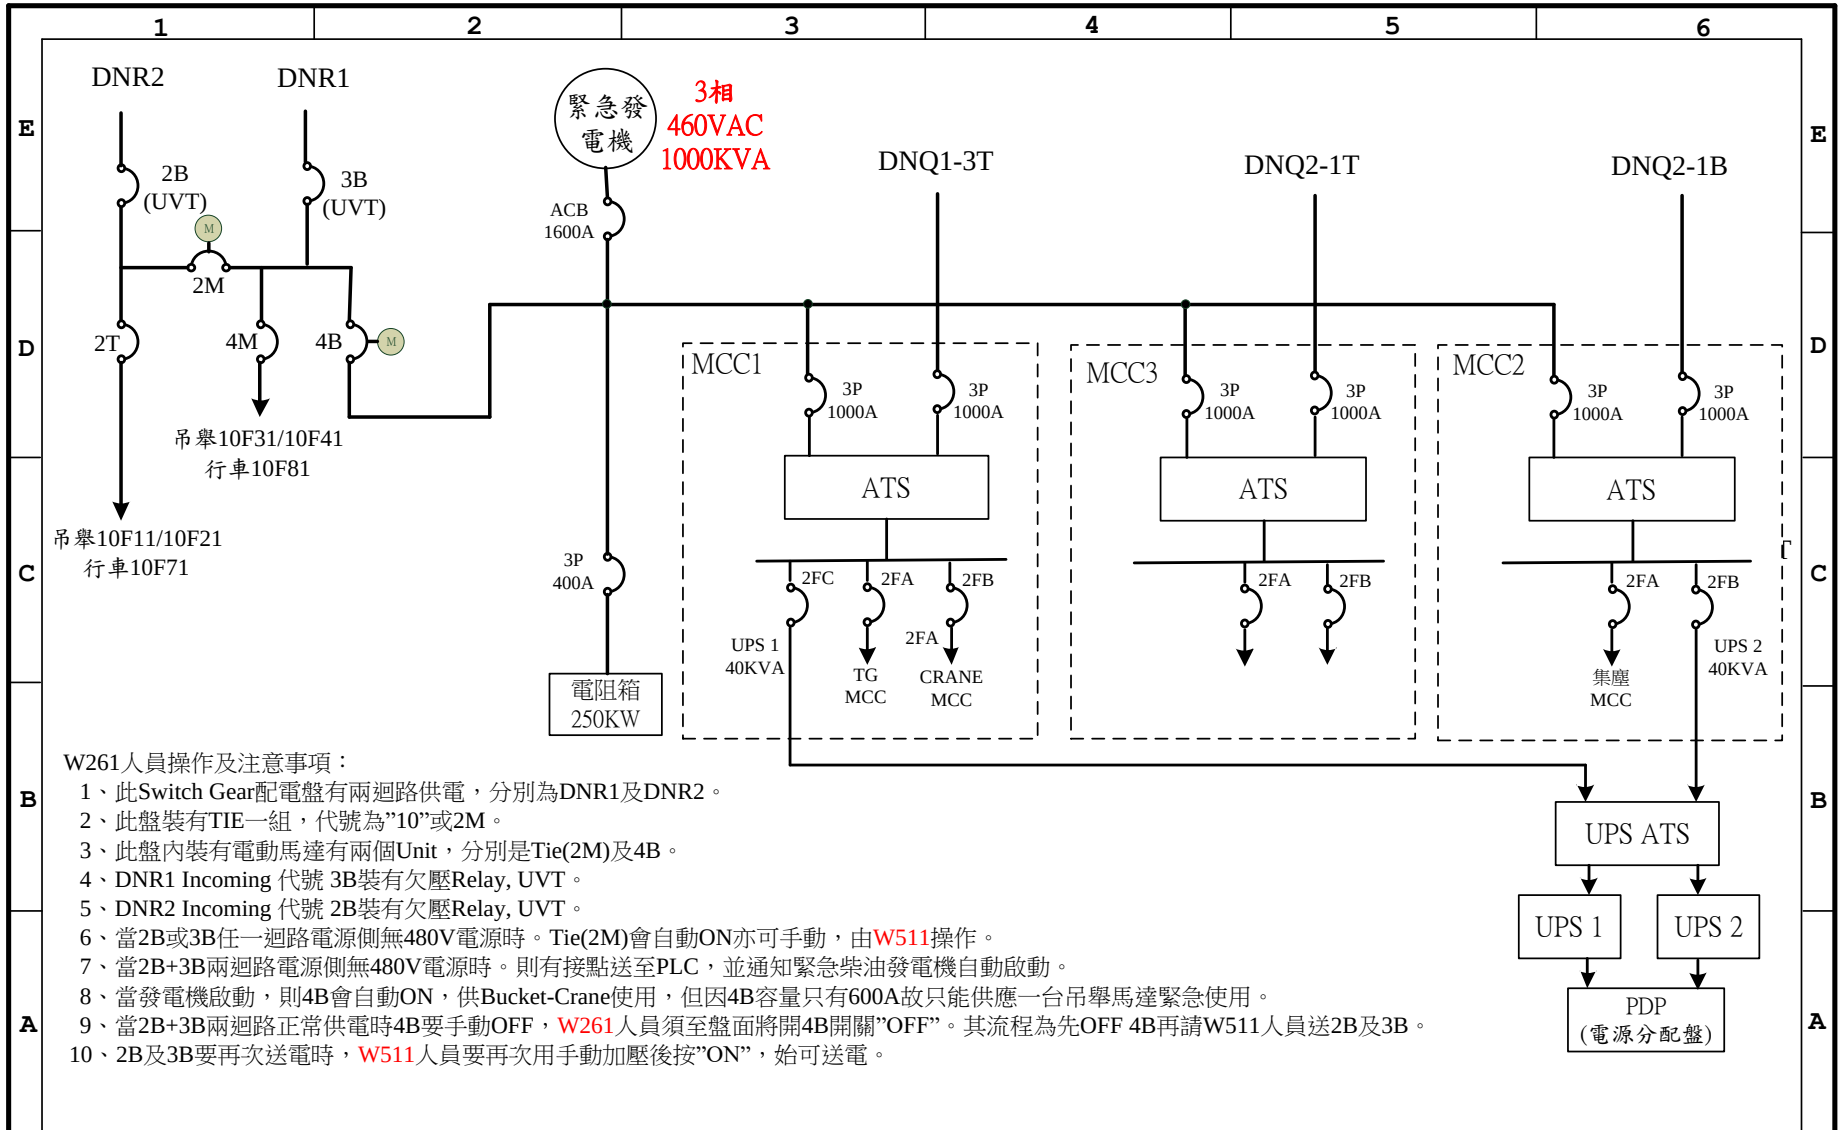

MANUFACTURE OR DESIGNER

W261



中國鋼鐵公司

CHINA STEEL CORPORATION
TAIWAN R.O.C

REV.	DATE	DESCRIPTION

TITLE:

PH3 CDQ緊急供電系統單線圖

DRAWN

DESIGNED

CHECKED

APPROVED

PHASE 34 COKE OVEN PLANT


DRAWING NO.

SHEET NO.

FILE NAME:



PH4 CDQ緊急電源系統

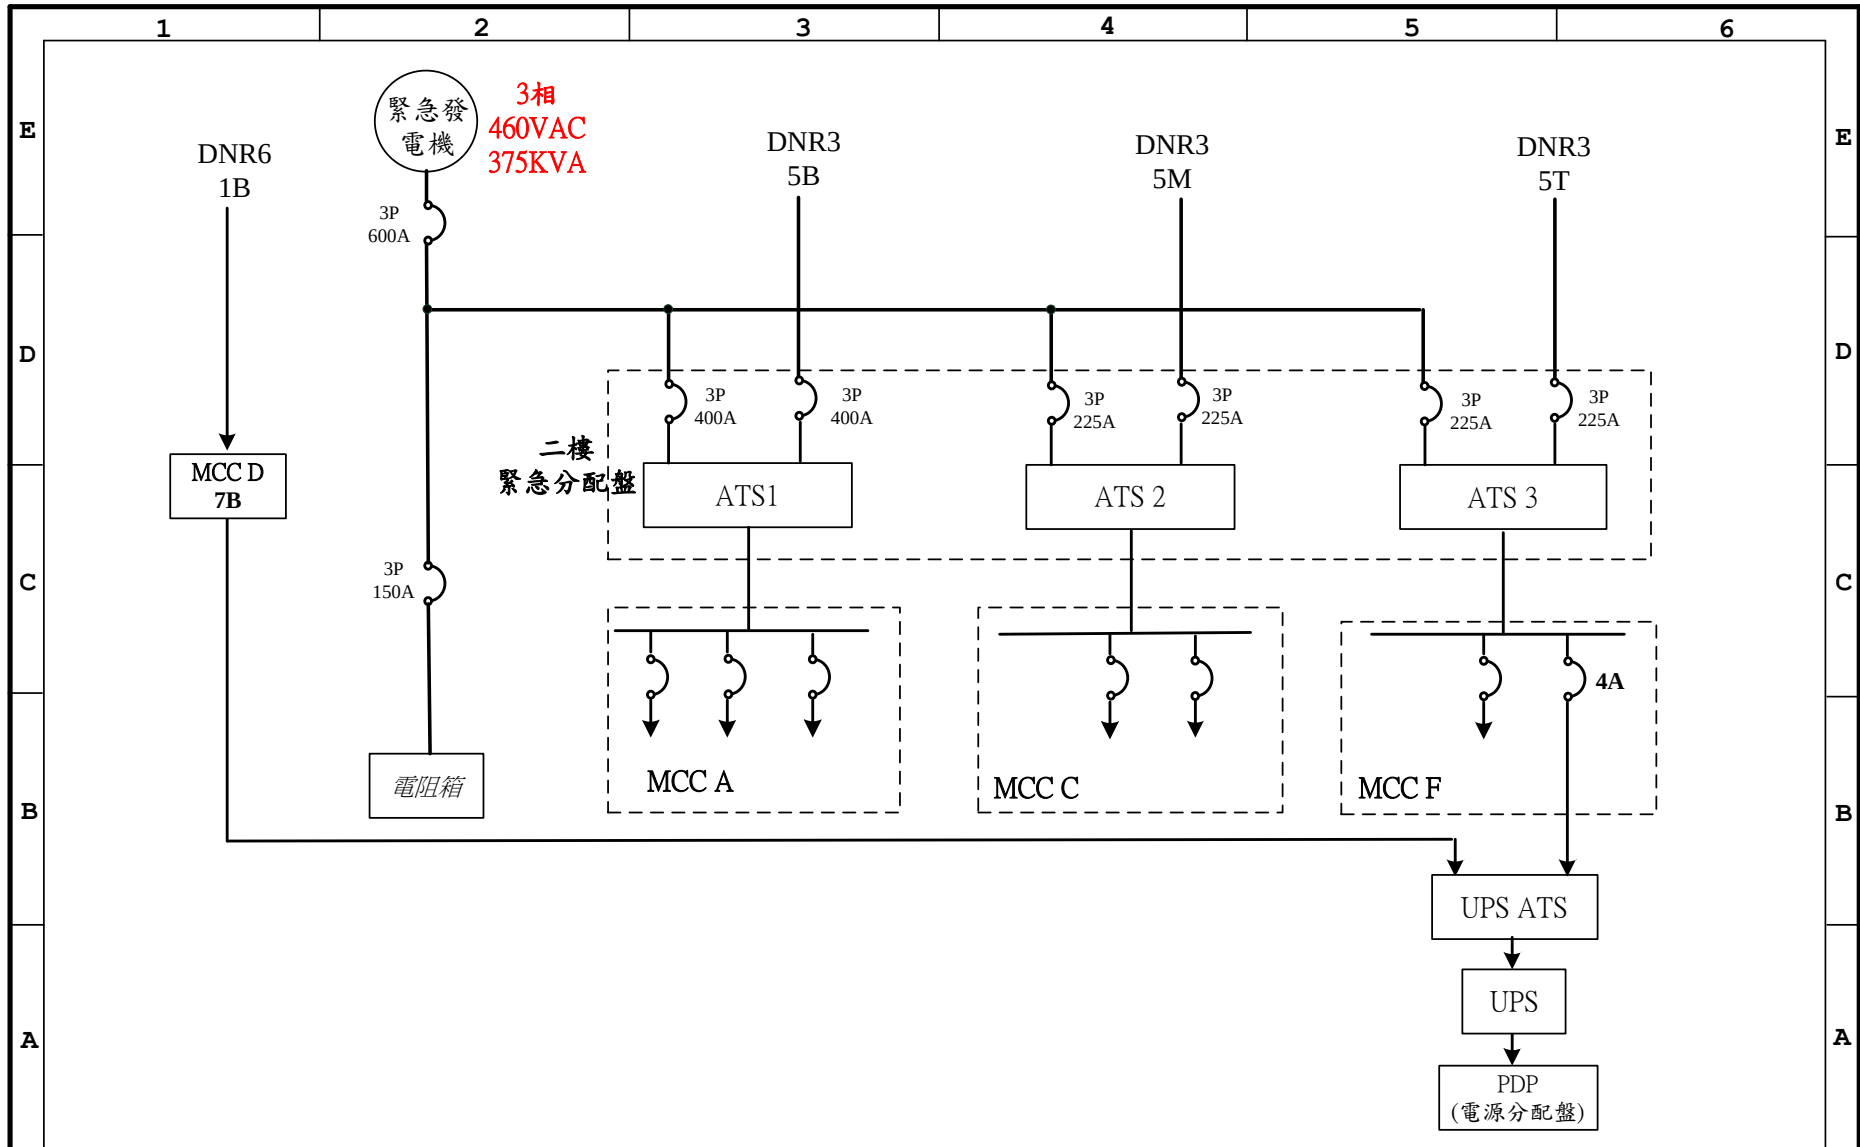

MANUFACTURE OR DESIGNER

W261



中國鋼鐵公司

CHINA STEEL CORPORATION
TAIWAN R.O.C

REV.

DATE

DESCRIPTION

TITLE:

PH4 CDQ緊急供電系統單線圖

DRAWN

DESIGNED

CHECKED

APPROVED

PHASE 34 COKE OVEN PLANT

DRAWING NO.

SHEET NO.

FILE NAME: